ANEXO 1
PLANO GENERAL CON UBICACION LOTE 23 MANZANA 2

NORTE

ESCALA 1:400

PLANO CATASTRAL

DEL LOTE 23 DE LA MANZANA 2 DEL FRACCIONAMIENTO FORESTA ETAPA I, CALLE CIRCUITO ALHELI NO. 7342. UBICADO EN MUNICIPIO, CIUDAD Y ESTADO DE CHIHUAHUA.

PROPIEDAD DE:

BANCO MONEX, SOCIEDAD ANONIMA, INSTITUCION DE BANCA MÚLTIPLE, MONEX GRUPO FINANCIERO FIDEICOMISO NO. F/10596

CLAVE CATASTRAL	447-359-023	MANZANA **2**	LOTE 23	SUPERFICIE DE TERRENO	234.00 M2
				SUPERFICIE CONSTRUIDA	0.00 M2
CLAVE CATASTRAL ESTANDAR	**08-001-019-00-0001-447-359-00023-00-0000**				

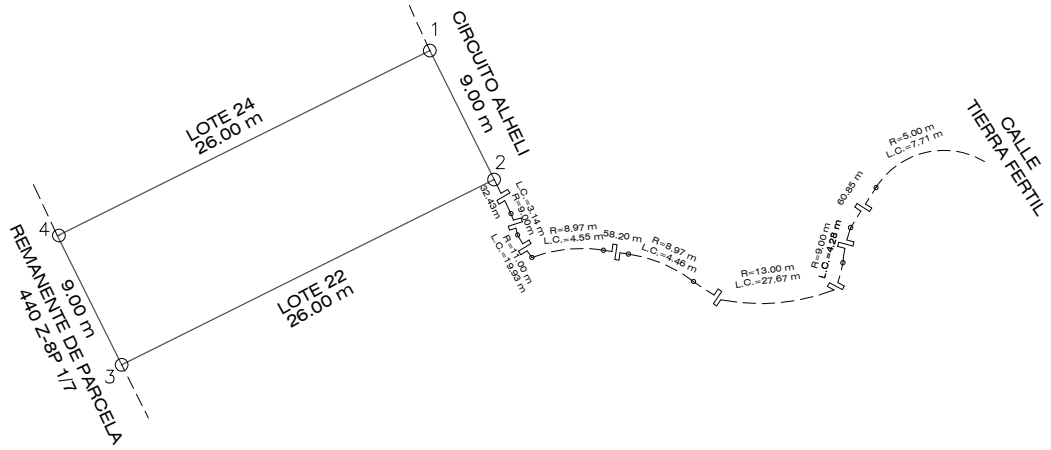

CUADRO DE CONSTRUCCION

LADO EST	LADO PV	RUMBO	DISTANCIA	V	COORDENADAS Y	COORDENADAS X
				1	3,170,639.68	385,760.41
1	2	S 26°27'43.53" E	9.00	2	3,170,631.62	385,764.42
2	3	S 63°32'16.47" W	26.00	3	3,170,620.03	385,741.14
3	4	N 26°27'43.53" W	9.00	4	3,170,628.09	385,737.13
4	1	N 63°32'16.47" E	26.00	1	3,170,639.68	385,760.41

SUPERFICIE = 234.00 m2

LOCALIZACIÓN

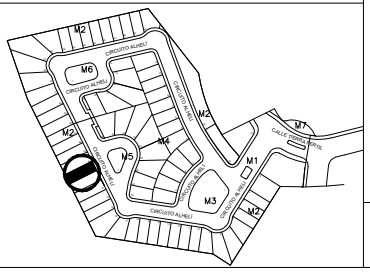

ING. JOSÉ LUIS RODRÍGUEZ HERNÁNDEZ
REG. P.C. No. 1899

CHIHUAHUA, CHIHUAHUA.
ENERO 2026