


ANEXO 1

PLANO GENERAL CON UBICACION LOTE 7 MANZANA 2

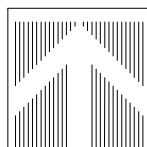

N O R T E

ESCALA 1:400

PLANO CATASTRAL


DEL LOTE 7 DE LA MANZANA 2 DEL FRACCIONAMIENTO
FORESTA ETAPA I, CALLE CIRCUITO ALHELI NO. 7310.

C H I H U A H U A .

PROPIEDAD DE:

BANCO MONEX, SOCIEDAD ANONIMA, INSTITUCION DE BANCA
MÚLTIPLE, MONEX GRUPO FINANCIERO FIDEICOMISO NO. F/10596

CLAVE CATASTRAL 447-359-007	MANZANA 2	LOTE 7	SUPERFICIE DE TERRENO	282.86 M2
			SUPERFICIE CONSTRUIDA	0.00 M2
CLAVE CATASTRAL ESTANDAR	08-001-019-00-0001-447-359-00007-00-0000			

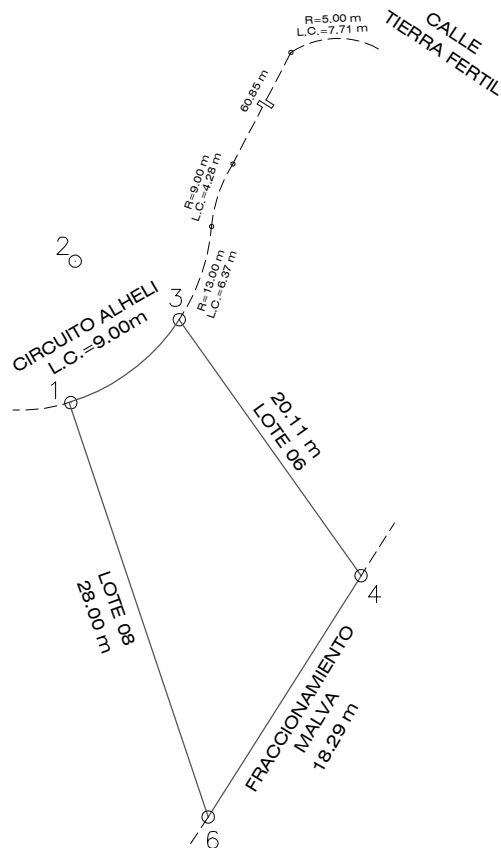


CUADRO DE CONSTRUCCION

LADO	EST	P.V.	RUMBO	DISTANCIA	V	C O O R D E N A D A S	
						Y	X
					1	3,170,578.40	385,872.23
1	3		N 53°03'22.63" E	8.82	3	3,170,583.70	385,879.28
			CENTRO DE CURVA		2	3,170,590.83	385,868.41
			DELTA = 39°39'58.71"	L.C.= 9.00			
			RADIO = 13.00	S.T.= 4.69			
3	4		S 35°24'09.29" E	20.11	4	3,170,567.31	385,890.93
4	6		S 32°21'39.37" W	18.29	6	3,170,551.86	385,881.14
6	1		N 18°33'13.91" W	28.00	1	3,170,578.40	385,872.23

SUPERFICIE = 282.86 m2

LOCALIZACIÓN

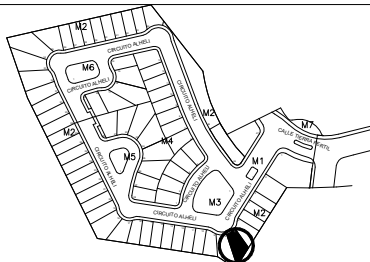

ING. JOSÉ LUIS RODRÍGUEZ HERNÁNDEZ
REG. P.C. No. 1899

CHIHUAHUA, CHIHUAHUA.
ENERO 2026