


ANEXO 1

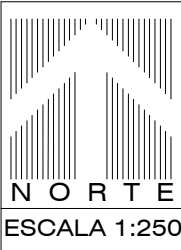


PLANO CATASTRAL

DEL LOTE 14 DE LA MANZANA 4 DEL FRACCIONAMIENTO FORESTA ETAPA 2, CALLE CIRCUITO ALHELI NO. 7359 UBICADO EN MUNICIPIO, CIUDAD Y ESTADO DE CHIHUAHUA.


PROPIEDAD DE:
BANCO MONEX, SOCIEDAD ANONIMA, INSTITUCION DE BANCA MÚLTIPLE, MONEX GRUPO FINANCIERO FIDEICOMISO NO. F/10596

CLAVE CATASTRAL 447-361-014	MANZANA 4	LOTE 14	SUPERFICIE DE TERRENO	198.58 M2
			SUPERFICIE CONSTRUIDA	0.00 M2
CLAVE CATASTRAL Estandar 08-001-019-00-0001-447-361-00014-00-0000				

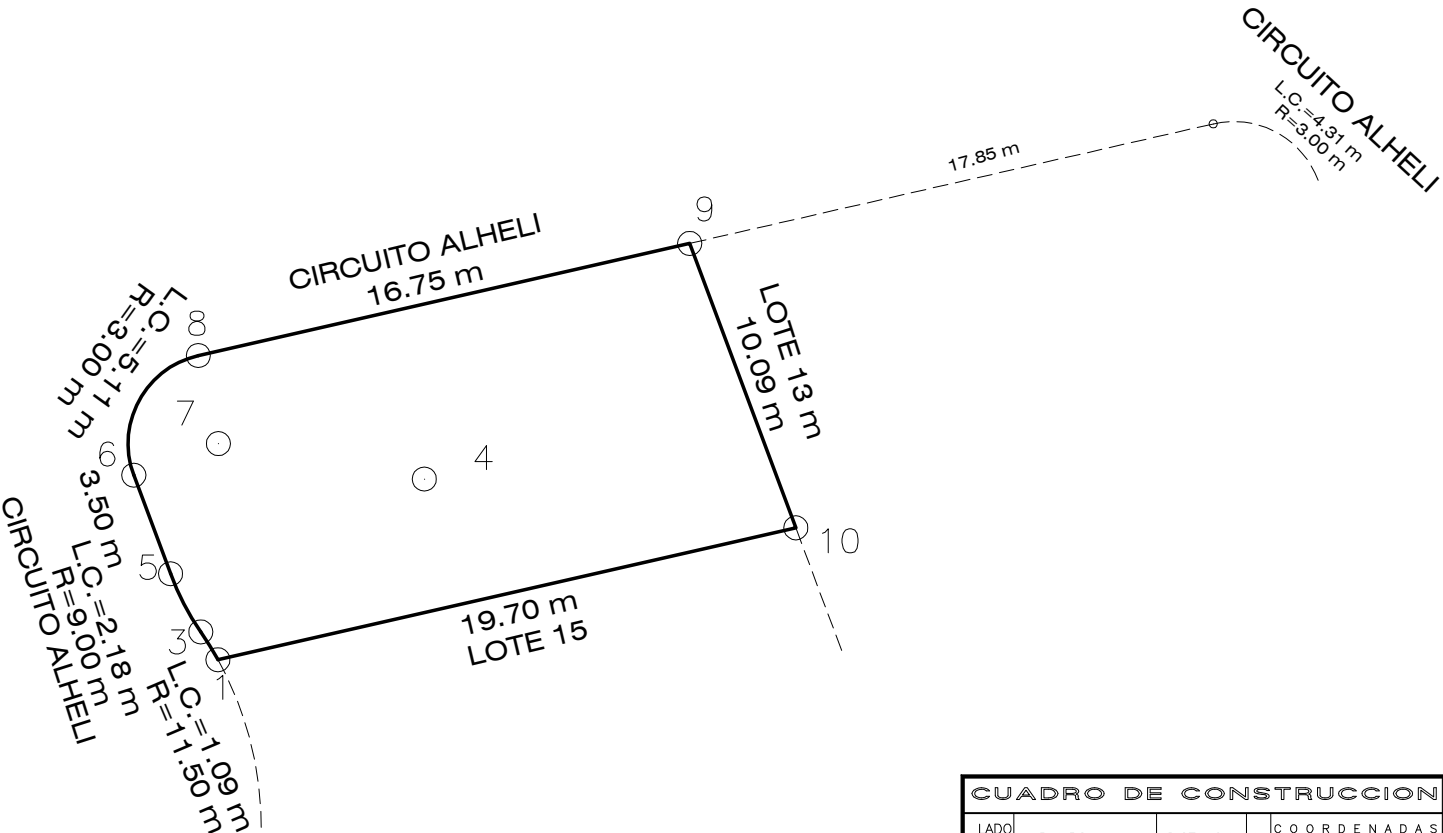

CUADRO DE CONSTRUCCION					
LADO	EST	PV	RUMBO	DISTANCIA	V
1	3		N 31°39'06.38" W CENTRO DE CURVA DELTA = 05°25'4.35" RADIO = 11.50	1.09 L.C.= 1.09 S.T.= 0.54	1 3,170,716.39
					3 3,170,717.32
					2 3,170,710.83
3	5		N 27°24'43.36" W CENTRO DE CURVA DELTA = 13°53'50.39" RADIO = 9.00	2.18 L.C.= 2.18 S.T.= 1.10	5 3,170,719.25
					4 3,170,722.40
5	6		N 20°27'48.17" W	3.50	6 3,170,722.53
6	8		N 28°20'20.45" E CENTRO DE CURVA DELTA = 97°36'17.23" RADIO = 3.00	4.51 L.C.= 5.11 S.T.= 3.43	8 3,170,726.50
					7 3,170,723.58
8	9		N 77°08'29.06" E	16.75	9 3,170,730.23
9	10		S 20°27'48.17" E	10.09	10 3,170,720.78
10	1		S 77°08'29.06" W	19.70	1 3,170,716.39
SUPERFICIE = 198.58 m2					

LOCALIZACIÓN

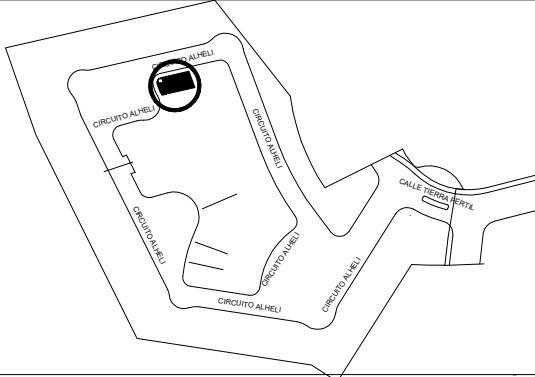

ING. JOSÉ LUIS RODRÍGUEZ HERNÁNDEZ
REG. P.C. No. 1899

CHIHUAHUA, CHIHUAHUA.
MARZO 2026