


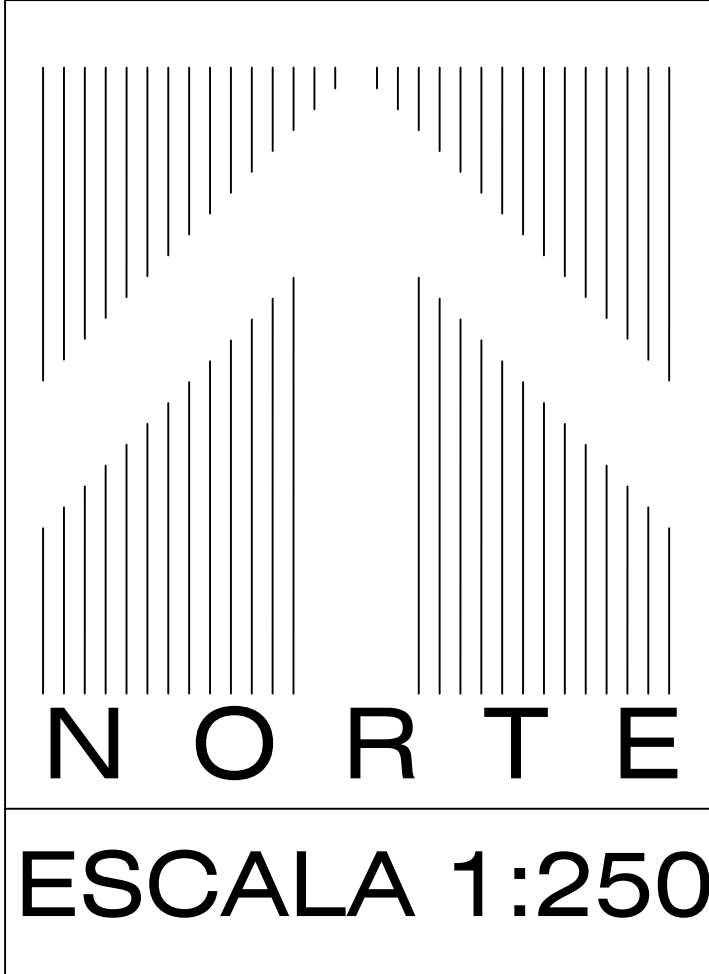

PLANO CATASTRAL


DEL LOTE 38 DE LA MANZANA 2 DEL FRACCIONAMIENTO
FORESTA ETAPA 2, CALLE CIRCUITO ALHELI NO. 7372
UBICADO EN MUNICIPIO, CIUDAD Y ESTADO DE
C H I H U A H U A .

PROPIEDAD DE:

BANCO MONEX, SOCIEDAD ANONIMA, INSTITUCION DE BANCA
MÚLTIPLE, MONEX GRUPO FINANCIERO FIDEICOMISO NO. F/10596


CLAVE CATASTRAL	447-359-038	MANZANA 2	LOTE 38	SUPERFICIE DE TERRENO	189.00 M2
				SUPERFICIE CONSTRUIDA	0.00 M2

CLAVE CATASTRAL Estandar 08-001-019-00-0001-447-359-00038-00-0000

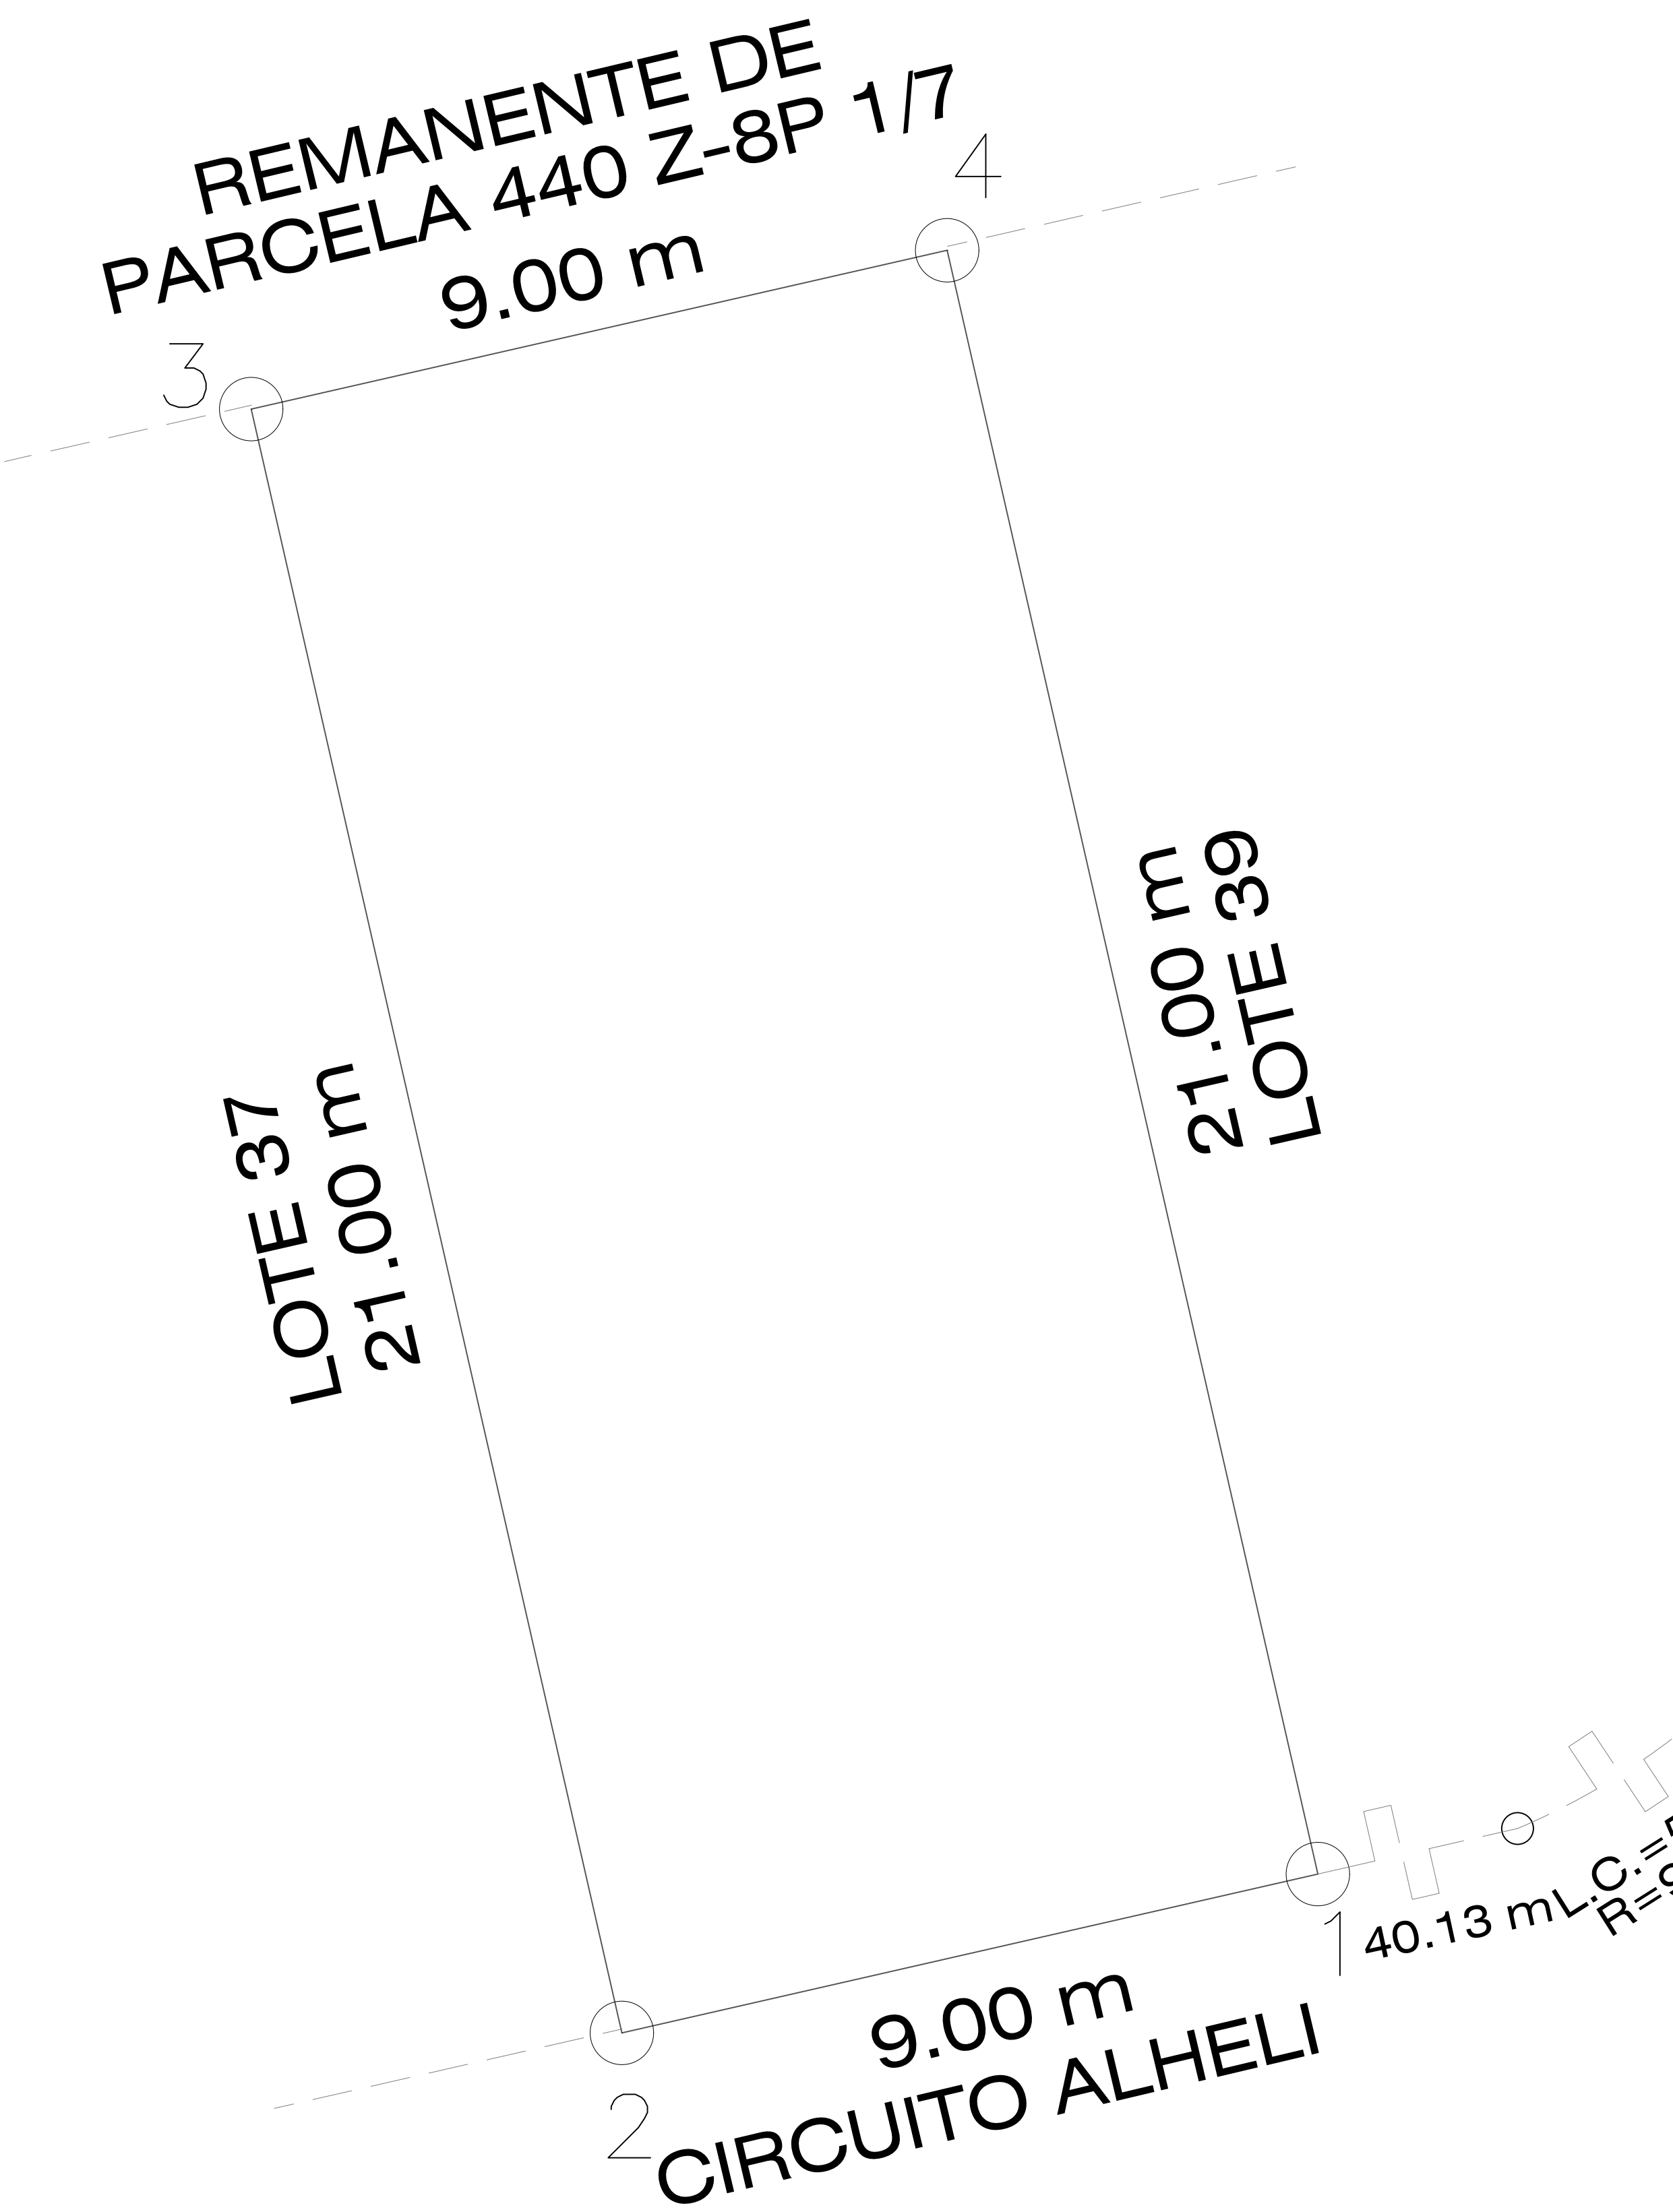

CUADRO DE CONSTRUCCION						
LADO		RUMBO	DISTANCIA	V	C O O R D E N A D A S	
EST	PV				Y	X
				1	3,170,739.34	385,761.71
1	2	S 77°08'29.06" W	9.00	2	3,170,737.34	385,752.94
2	3	N 12°51'30.94" W	21.00	3	3,170,757.81	385,748.27
3	4	N 77°08'29.06" E	9.00	4	3,170,759.81	385,757.04
4	1	S 12°51'30.94" E	21.00	1	3,170,739.34	385,761.71
SUPERFICIE = 189.00 m2						

LOCALIZACIÓN

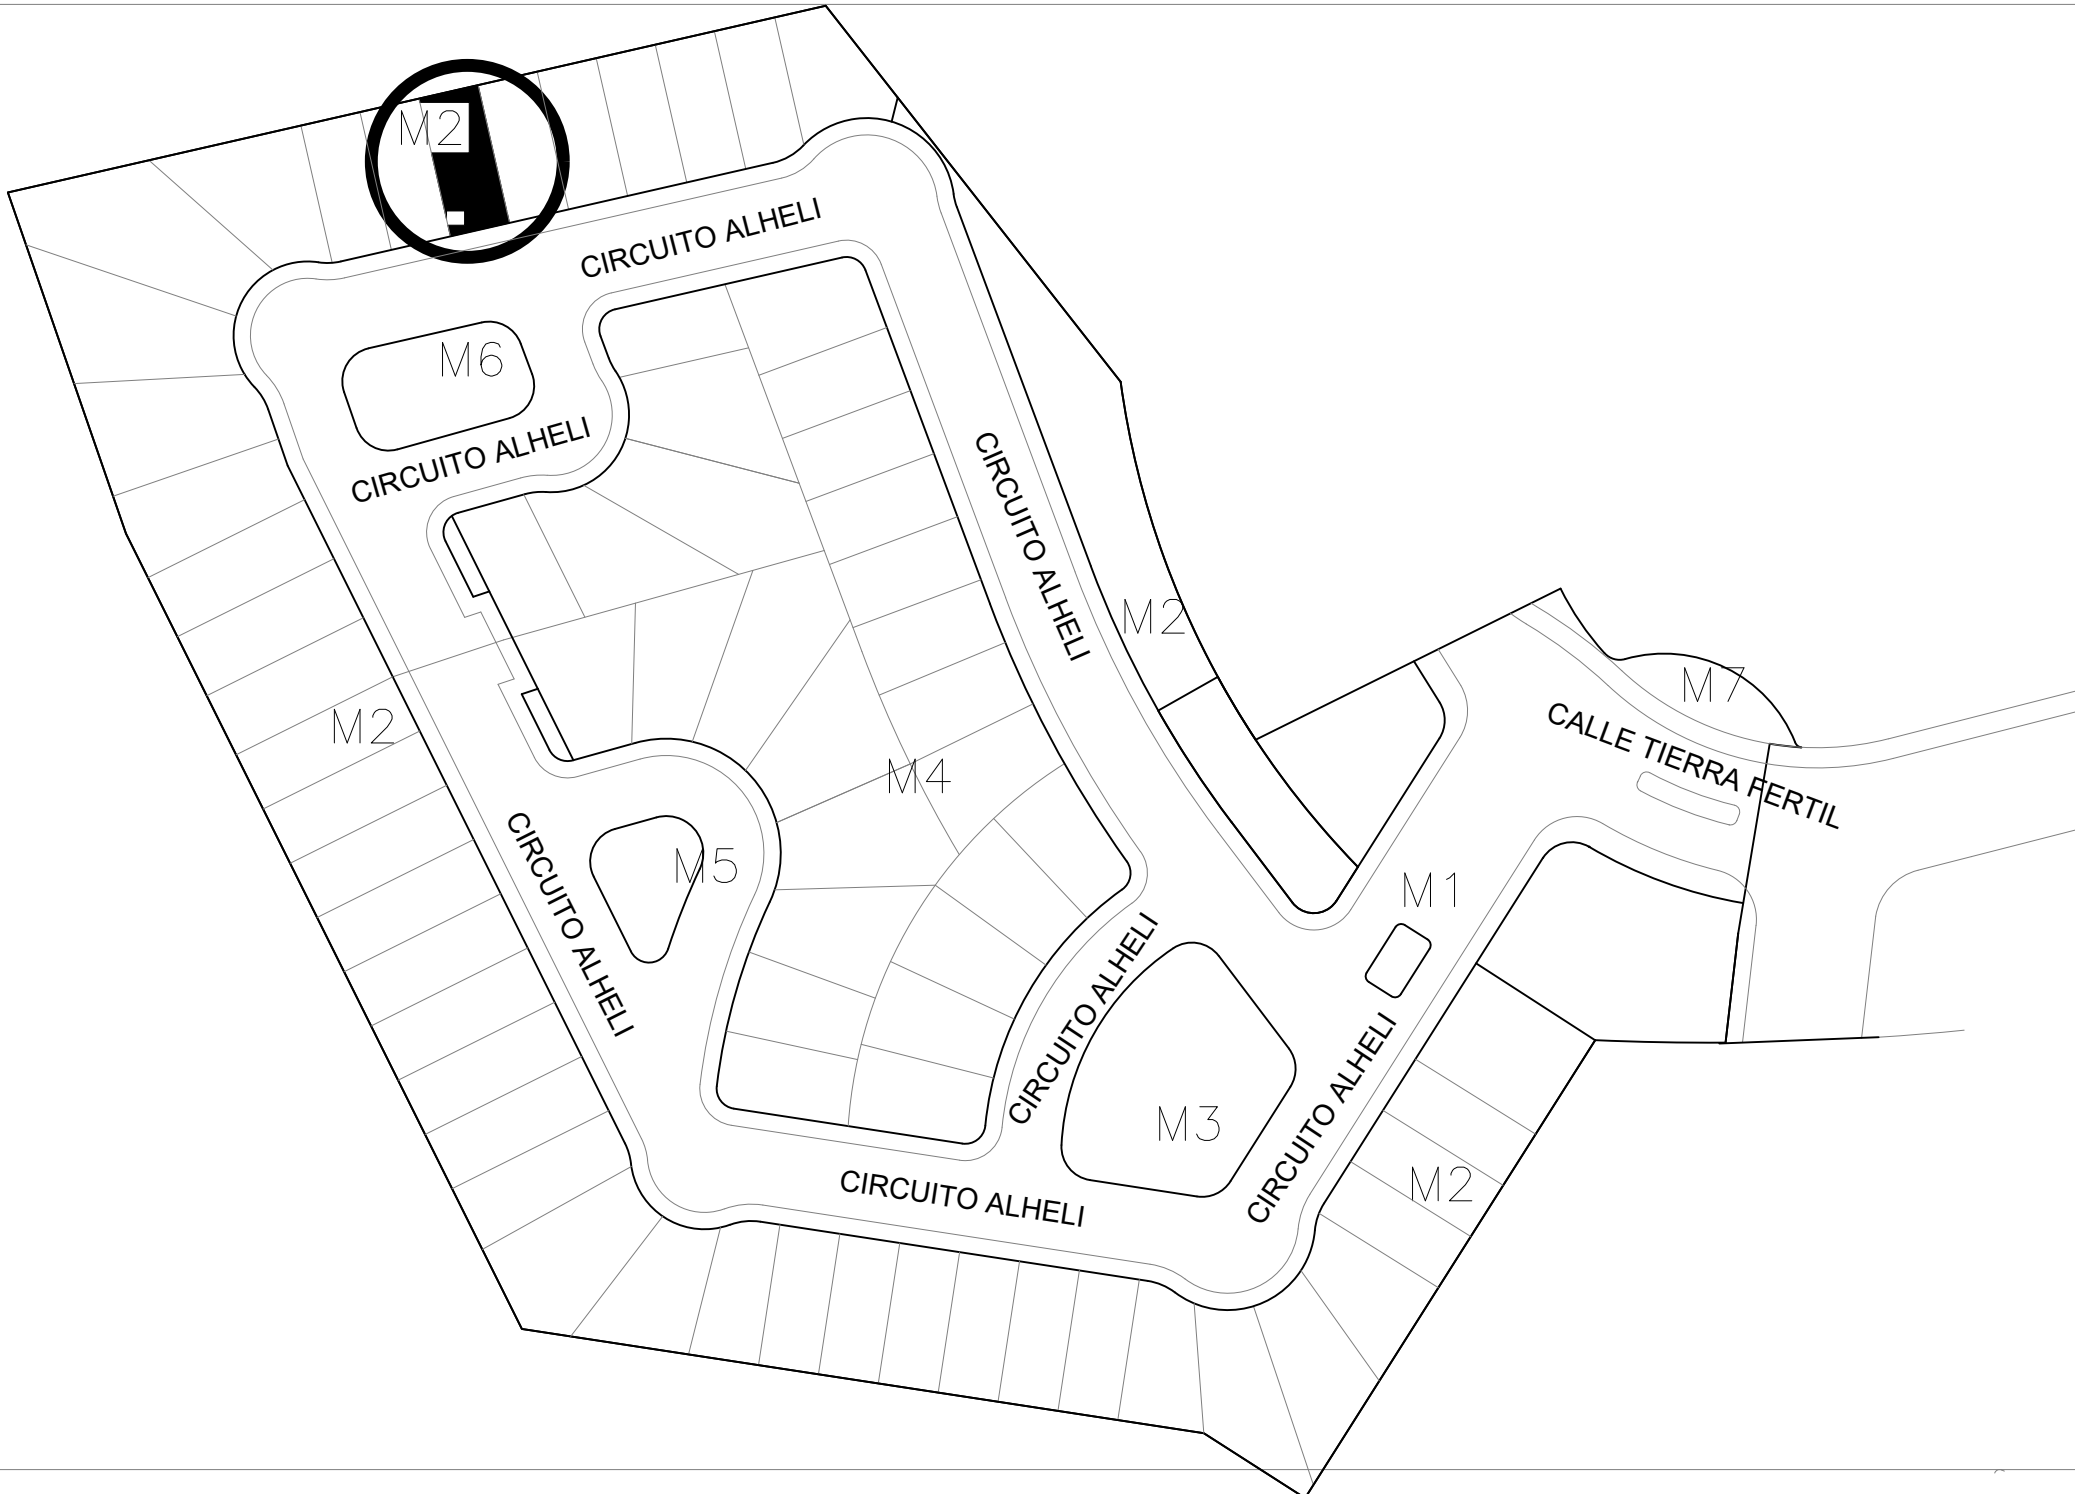

ING. JOSÉ LUIS RODRÍGUEZ HERNÁNDEZ
REG. P.C. No. 1899

CHIHUAHUA, CHIHUAHUA.
MARZO 2026