

ANEXO 1




PLANO CATASTRAL

DEL LOTE 40 DE LA MANZANA 2 DEL FRACCIONAMIENTO FORESTA ETAPA 2, CALLE CIRCUITO ALHELI NO. 7376 UBICADO EN MUNICIPIO, CIUDAD Y ESTADO DE CHIHUAHUA.


PROPIEDAD DE:
BANCO MONEX, SOCIEDAD ANONIMA, INSTITUCION DE BANCA MÚLTIPLE, MONEX GRUPO FINANCIERO FIDEICOMISO NO. F/10596

CLAVE CATASTRAL 447-359-040	MANZANA 2	LOTE 40	SUPERFICIE DE TERRENO	189.00 M2
			SUPERFICIE CONSTRUIDA	0.00 M2
CLAVE CATASTRAL Estandar	08-001-019-00-0001-447-359-00040-00-0000			

CUADRO DE CONSTRUCCION						
LADO		RUMBO	DISTANCIA	V	COORDENADAS	
EST	PV				Y	X
				1	3,170,743.34	385,779.26
1	2	S 77°08'29.06" W	9.00	2	3,170,741.34	385,770.49
2	3	N 12°51'30.94" W	21.00	3	3,170,761.81	385,765.81
3	4	N 77°08'29.06" E	9.00	4	3,170,763.82	385,774.59
4	1	S 12°51'30.94" E	21.00	1	3,170,743.34	385,779.26
SUPERFICIE = 189.00 m2						

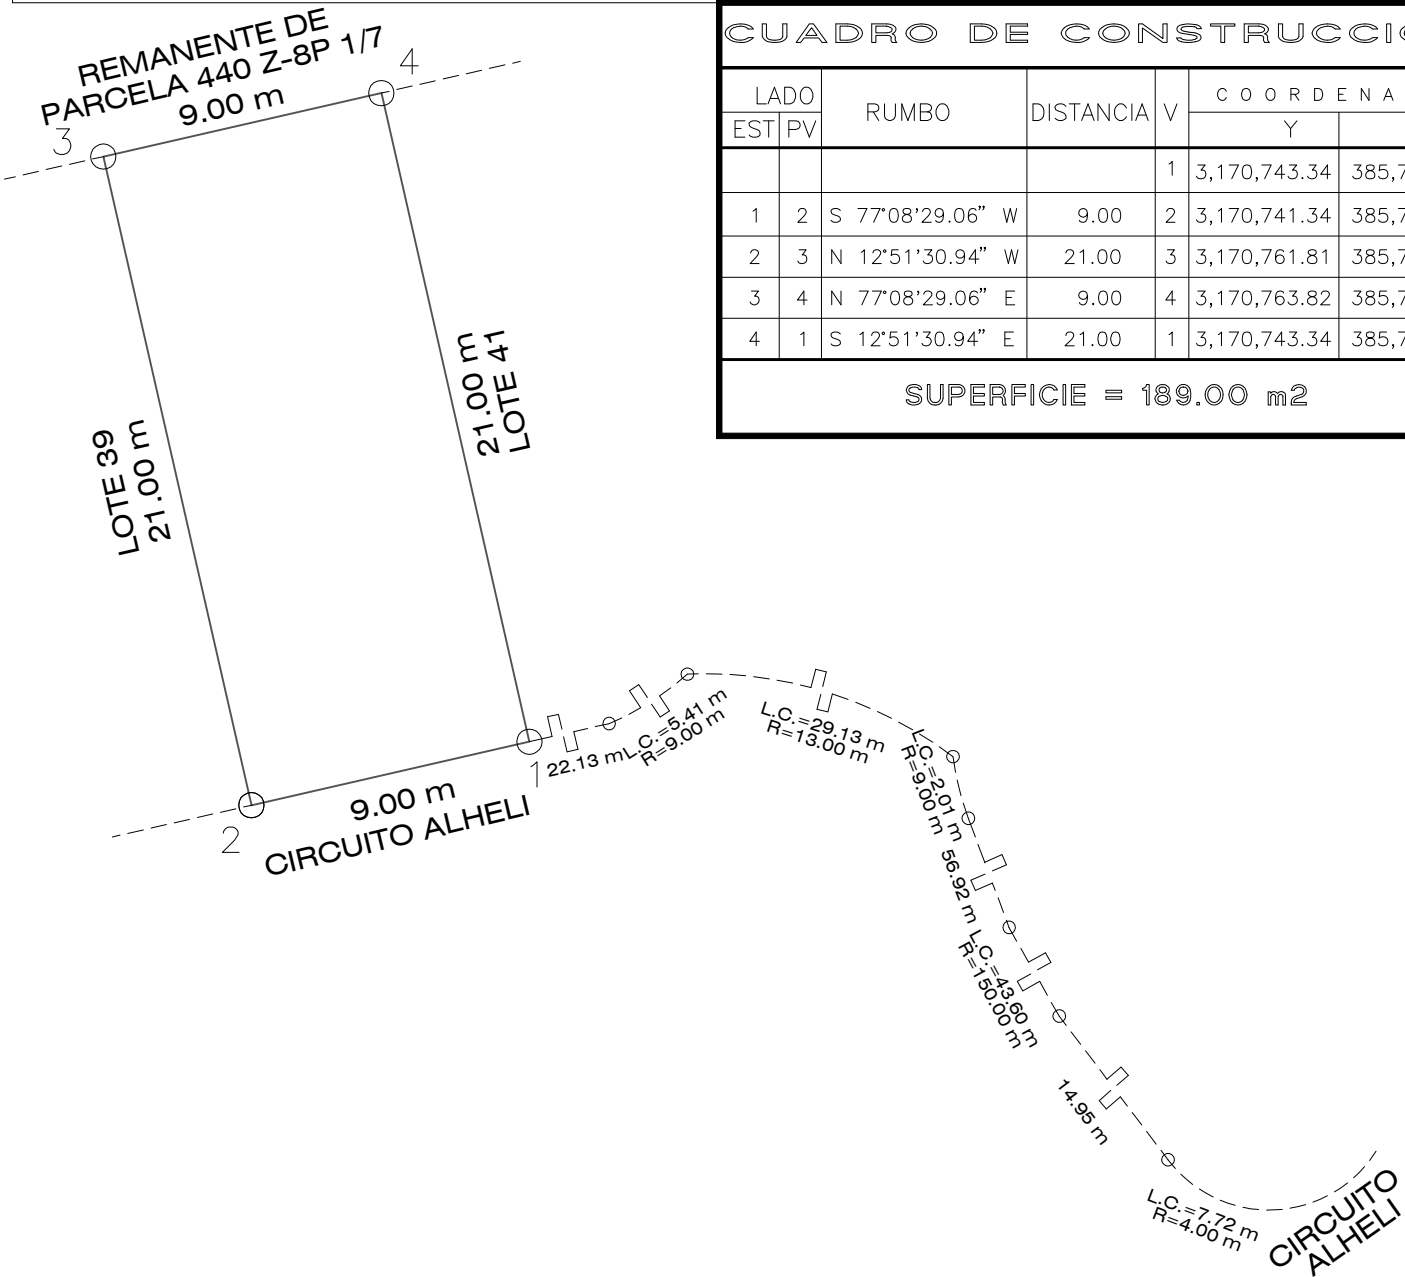

LOCALIZACIÓN

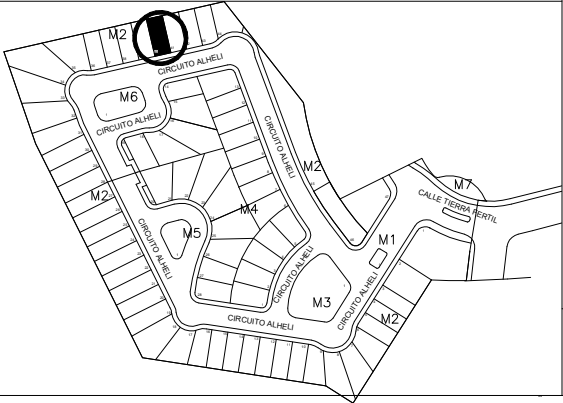

ING. JOSÉ LUIS RODRÍGUEZ HERNÁNDEZ
REG. P.C. No. 1899

CHIHUAHUA, CHIHUAHUA.
MARZO 2026