


ANEXO 1
PLANO GENERAL CON UBICACION LOTE 21 MANZANA 2

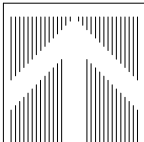

N O R T E
ESCALA 1:400


PLANO CATASTRAL

DEL LOTE 21 DE LA MANZANA 2 DEL FRACCIONAMIENTO
FORESTA ETAPA I, CALLE CIRCUITO ALHELI NO. 7338.
UBICADO EN MUNICIPIO, CIUDAD Y ESTADO DE
C H I H U A H U A .

PROPIEDAD DE:

BANCO MONEX, SOCIEDAD ANONIMA, INSTITUCION DE BANCA
MÚLTIPLE, MONEX GRUPO FINANCIERO FIDEICOMISO NO. F/10596

CLAVE CATASTRAL	447-359-021	MANZANA 2	LOTE 21	SUPERFICIE DE TERRENO	234.00 M2
				SUPERFICIE CONSTRUIDA	0.00 M2
CLAVE CATASTRAL ESTANDAR	08-001-019-00-0001-447-359-00021-00-0000				

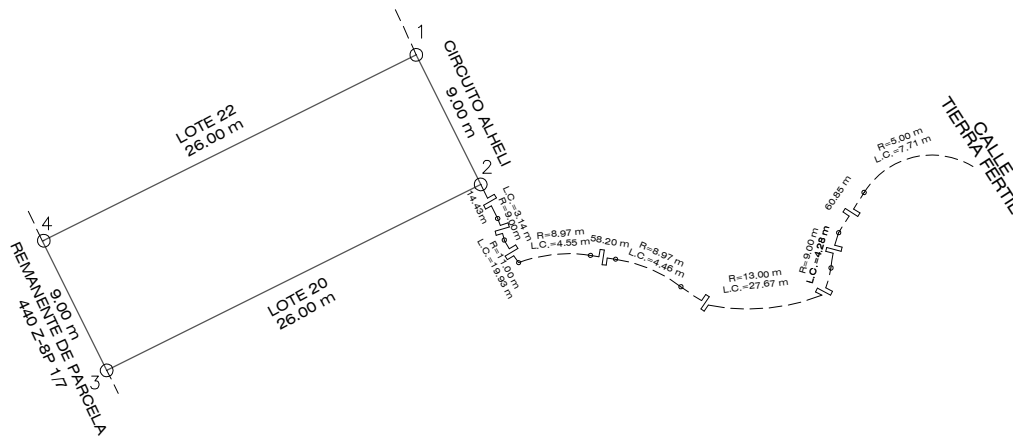


CUADRO DE CONSTRUCCION

LADO EST	PV	RUMBO	DISTANCIA	V	C O O R D E N A D A S	
					Y	X
				1	3,170,623.56	385,768.43
1	2	S 26°27'43.53" E	9.00	2	3,170,615.51	385,772.44
2	3	S 63°32'16.47" W	26.00	3	3,170,603.92	385,749.16
3	4	N 26°27'43.53" W	9.00	4	3,170,611.98	385,745.15
4	1	N 63°32'16.47" E	26.00	1	3,170,623.56	385,768.43

SUPERFICIE = 234.00 m2

LOCALIZACIÓN

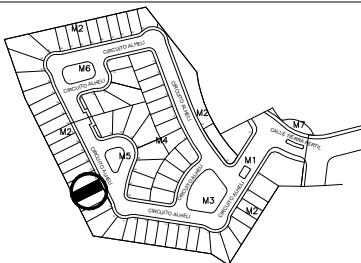

ING. JOSÉ LUIS RODRÍGUEZ HERNÁNDEZ
REG. P.C. No. 1899

CHIHUAHUA, CHIHUAHUA.
ENERO 2026