


ANEXO 1
PLANO GENERAL CON UBICACION LOTE 22 MANZANA 2

 N O R T E ESCALA 1:400	P L A N O C A T A S T R A L							
	DEL LOTE 22 DE LA MANZANA 2 DEL FRACCIONAMIENTO FORESTA ETAPA I, CALLE CIRCUITO ALHELI NO. 7340. UBICADO EN MUNICIPIO, CIUDAD Y ESTADO DE C H I H U A H U A .							
PROPIEDAD DE: BANCO MONEX, SOCIEDAD ANONIMA, INSTITUCION DE BANCA MÚLTIPLE, MONEX GRUPO FINANCIERO FIDEICOMISO NO. F/10596								
CLAVE CATASTRAL 447-359-022		MANZANA 2	LOTE 22	<table border="1" style="width: 100%; border-collapse: collapse;"><tr><td style="width: 50%;">SUPERFICIE DE TERRENO</td><td style="width: 50%;">234.00 M2</td></tr><tr><td>SUPERFICIE CONSTRUIDA</td><td>0.00 M2</td></tr></table>	SUPERFICIE DE TERRENO	234.00 M2	SUPERFICIE CONSTRUIDA	0.00 M2
SUPERFICIE DE TERRENO	234.00 M2							
SUPERFICIE CONSTRUIDA	0.00 M2							
CLAVE CATASTRAL ESTANDAR 08-001-019-00-0001-447-359-00022-00-0000								

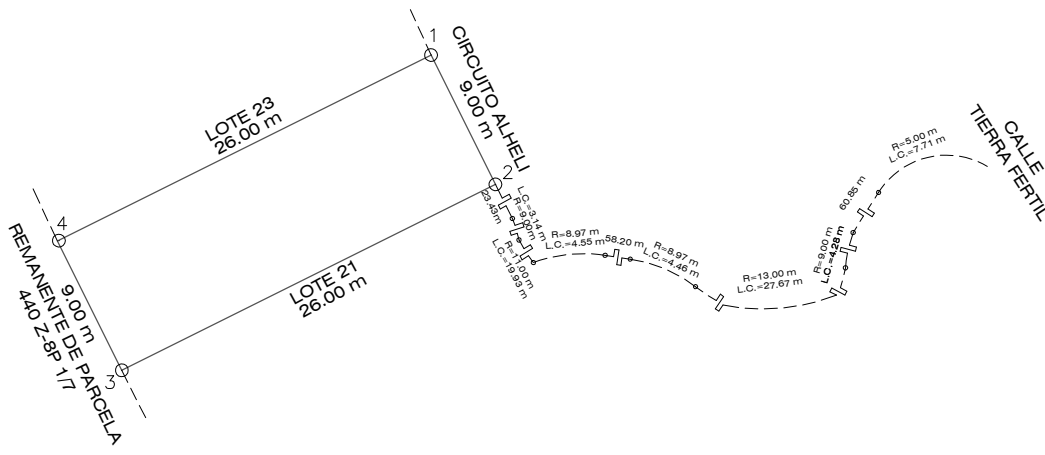

CUADRO DE CONSTRUCCION							
LADO		RUMBO	DISTANCIA	V	C O O R D E N A D A S		
EST	PV				Y	X	
				1	3,170,631.62	385,764.42	
1	2	S 26°27'43.53" E	9.00	2	3,170,623.56	385,768.43	
2	3	S 63°32'16.47" W	26.00	3	3,170,611.98	385,745.15	
3	4	N 26°27'43.53" W	9.00	4	3,170,620.03	385,741.14	
4	1	N 63°32'16.47" E	26.00	1	3,170,631.62	385,764.42	
SUPERFICIE = 234.00 m2							

