


## ANEXO 1

 

ESCALA 1:250


# PLANO CATASTRAL

DEL LOTE 25 DE LA MANZANA 4 DEL FRACCIONAMIENTO  
FORESTA ETAPA 1, CALLE CIRCUITO ALHELI NO. 7337.  
UBICADO EN MUNICIPIO, CIUDAD Y ESTADO DE  
C H I H U A H U A .

**PROPIEDAD DE:**

BANCO MONEX, SOCIEDAD ANONIMA, INSTITUCION DE BANCA  
MÚLTIPLE, MONEX GRUPO FINANCIERO FIDEICOMISO NO. F/10596

|                                                                          |                  |                |                       |           |
|--------------------------------------------------------------------------|------------------|----------------|-----------------------|-----------|
| CLAVE CATASTRAL <b>447-361-025</b>                                       | MANZANA <b>4</b> | LOTE <b>25</b> | SUPERFICIE DE TERRENO | 347.90 M2 |
|                                                                          |                  |                | SUPERFICIE CONSTRUIDA | 0.00 M2   |
| CLAVE CATASTRAL Estandar <b>08-001-019-00-0001-447-361-00025-00-0000</b> |                  |                |                       |           |

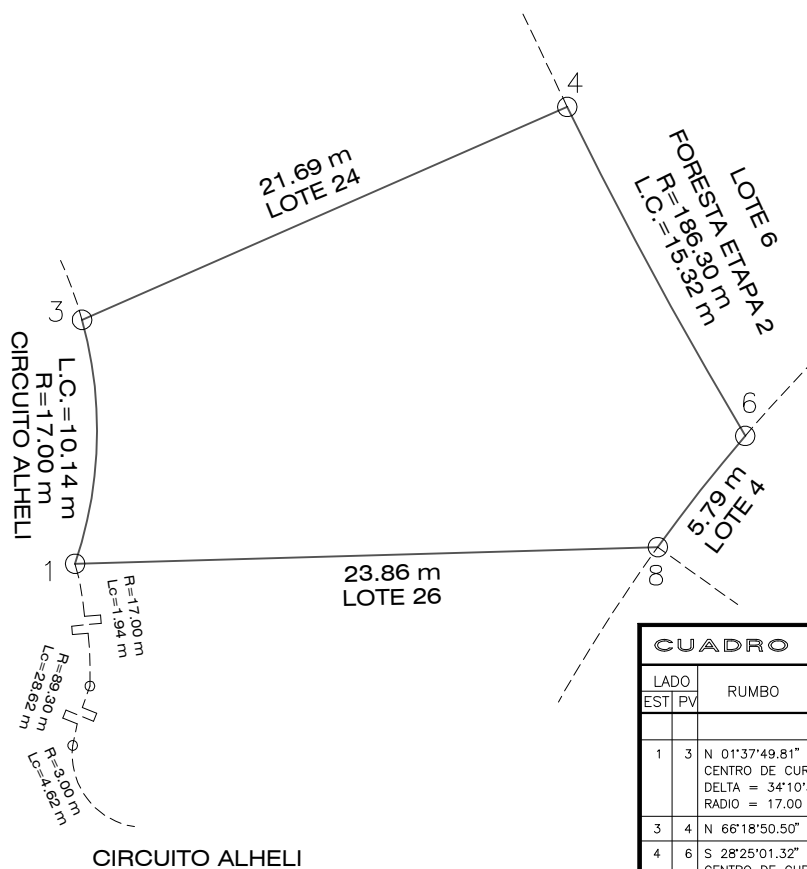


### CUADRO DE CONSTRUCCION

| LADO<br>EST. PV |   | RUMBO                                                                         | DISTANCIA                                | V | C O O R D E N A D A S |            |
|-----------------|---|-------------------------------------------------------------------------------|------------------------------------------|---|-----------------------|------------|
|                 |   |                                                                               |                                          |   | Y                     | X          |
|                 |   |                                                                               |                                          | 1 | 3,170,640.26          | 385,801.10 |
| 1               | 3 | N 01°37'49.81" E<br>CENTRO DE CURVA<br>DELTA = 34°10'38.27"<br>RADIO = 17.00  | 9.99<br><br>L.C. = 10.14<br>S.T. = 5.23  | 3 | 3,170,650.25          | 385,801.39 |
|                 |   |                                                                               |                                          | 2 | 3,170,645.72          | 385,785.00 |
| 3               | 4 | N 66°18'50.50" E                                                              | 21.69                                    | 4 | 3,170,658.96          | 385,821.25 |
| 4               | 6 | S 28°25'01.32" E<br>CENTRO DE CURVA<br>DELTA = 04°42'36.93"<br>RADIO = 186.32 | 15.31<br><br>L.C. = 15.32<br>S.T. = 7.66 | 6 | 3,170,645.50          | 385,828.54 |
|                 |   |                                                                               |                                          | 5 | 3,170,740.81          | 385,988.61 |
| 6               | 8 | S 38°11'55.04" W<br>CENTRO DE CURVA<br>DELTA = 04°47'12.67"<br>RADIO = 69.30  | 5.79<br><br>L.C. = 5.79<br>S.T. = 2.90   | 8 | 3,170,640.95          | 385,824.96 |
|                 |   |                                                                               |                                          | 7 | 3,170,600.41          | 385,881.16 |
| 8               | 1 | S 88°21'16.65" W                                                              | 23.86                                    | 1 | 3,170,640.26          | 385,801.10 |

**SUPERFICIE = 347.90 m2**

## LOCALIZACIÓN

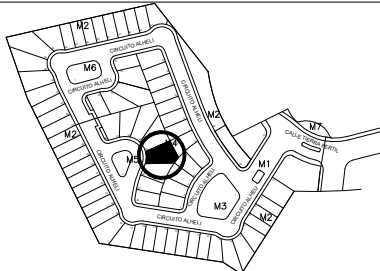

ING. JOSÉ LUIS RODRÍGUEZ HERNÁNDEZ  
REG. P.C. No. 1899

CHIHUAHUA, CHIHUAHUA.  
MARZO 2026