


# ANEXO 1


## PLANO GENERAL CON UBICACION LOTE 8 MANZANA 2

|   |   |           |        |                                                                  |
|---|---|-----------|--------|------------------------------------------------------------------|
| <br><b>NORTE</b><br>ESCALA 1:300                       | <h3>PLANO CATASTRAL</h3>   |           |        |                                                                  |
|   | DEL LOTE 8 DE LA MANZANA 2 DEL FRACCIONAMIENTO<br>FORESTA ETAPA I, CALLE CIRCUITO ALHELI NO. 7312.<br>UBICADO EN MUNICIPIO, CIUDAD Y ESTADO DE<br>C H I H U A H U A . |           |        |                                                                  |
| <b>PROPIEDAD DE:</b><br>BANCO MONEX, SOCIEDAD ANONIMA, INSTITUCION DE BANCA<br>MÚLTIPLE, MONEX GRUPO FINANCIERO FIDEICOMISO NO. F/10596 |   |           |        |                                                                  |
| CLAVE CATASTRAL   | 447-359-008   | MANZANA 2 | LOTE 8 | SUPERFICIE DE TERRENO 282.73 M2<br>SUPERFICIE CONSTRUIDA 0.00 M2 |
| CLAVE CATASTRAL Estandar   | 08-001-019-00-0001-447-359-00008-00-0000   |           |        |                                                                  |

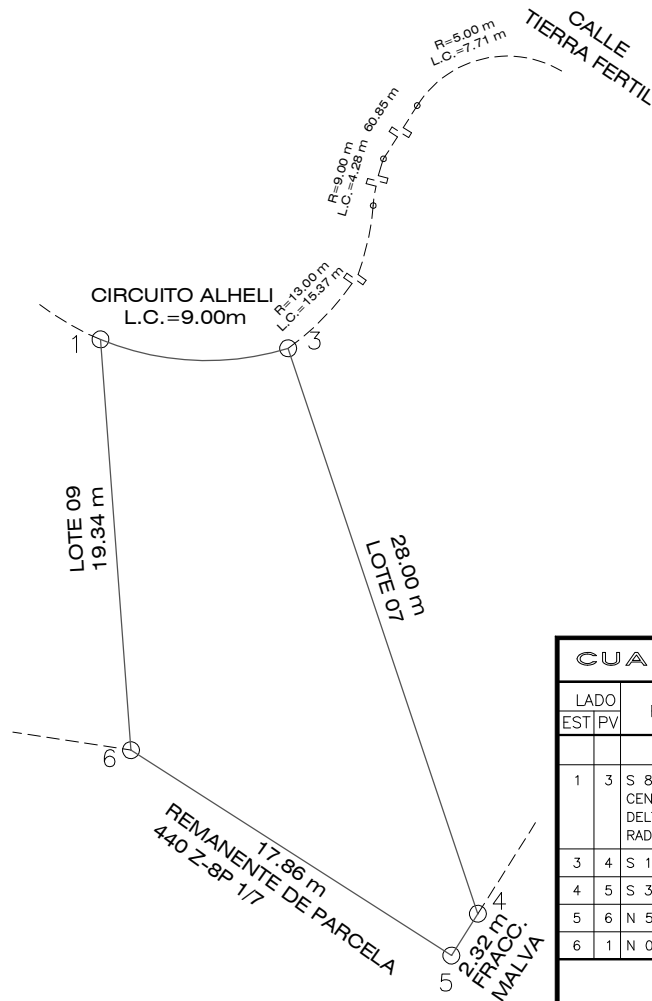

| CUADRO DE CONSTRUCCION |     |    |                                          |                            |   |                         |
|------------------------|-----|----|------------------------------------------|----------------------------|---|-------------------------|
| LADO                   | EST | PV | RUMBO                                    | DISTANCIA                  | V | COORDENADAS             |
|                        |     |    |                                          |                            |   | Y X                     |
| 1                      | 3   |    | S 87°16'38.66\"                          | 8.82                       | 3 | 3,170,578.82 385,872.23 |
| 2                      |     |    | CENTRO DE CURVA<br>DELTA = 39°39'58.71\" | L.C. = 9.00<br>S.T. = 4.69 | 2 | 3,170,590.83 385,868.41 |
| 3                      | 4   |    | S 18°33'13.92\"                          | 28.00                      | 4 | 3,170,551.86 385,881.14 |
| 4                      | 5   |    | S 32°21'39.54\"                          | 2.32                       | 5 | 3,170,549.90 385,879.90 |
| 5                      | 6   |    | N 57°20'47.09\"                          | 17.86                      | 6 | 3,170,559.54 385,864.86 |
| 6                      | 1   |    | N 04°15'34.52\"                          | 19.34                      | 1 | 3,170,578.82 385,863.42 |
| SUPERFICIE = 282.73 m2 |     |    |                                          |                            |   |                         |

### LOCALIZACIÓN

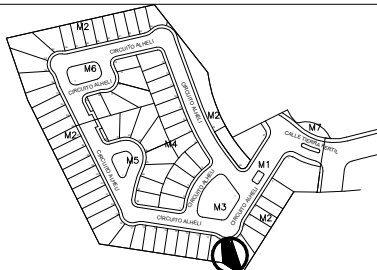

ING. JOSÉ LUIS RODRÍGUEZ HERNÁNDEZ  
REG. P.C. No. 1899

CHIHUAHUA, CHIHUAHUA.  
ENERO 2026