

ANEXO 1
PLANO GENERAL CON UBICACION LOTE 9 MANZANA 2



N O R T E
ESCALA 1:250

PLANO CATASTRAL


DEL LOTE 9 DE LA MANZANA 2 DEL FRACCIONAMIENTO
FORESTA ETAPA I, CALLE CIRCUITO ALHELI NO. 7314.
UBICADO EN MUNICIPIO, CIUDAD Y ESTADO DE
C H I H U A H U A .

PROPIEDAD DE:


BANCO MONEX, SOCIEDAD ANONIMA, INSTITUCION DE BANCA
MÚLTIPLE, MONEX GRUPO FINANCIERO FIDEICOMISO NO. F/10596

CLAVE CATASTRAL 447-359-009	MANZANA 2	LOTE 9	SUPERFICIE DE TERRENO	215.31 M2
			SUPERFICIE CONSTRUIDA	0.00 M2
CLAVE CATASTRAL ESTANDAR 08-001-019-00-0001-447-359-00009-00-0000				

CUADRO DE CONSTRUCCION					
LADO	RUMBO	DISTANCIA	V	C O O R D E N A D A S	
EST/PV				Y	X
1	2	S 81°13'17.81" E	1.24	2	3,170,582.36
2	4	S 67°08'15.42" E	4.41	4	3,170,582.17
		CENTRO DE CURVA		3	3,170,573.30
		DELTA = 28°29'22.79"	L.C.= 4.46		385,855.27
		RADIO = 8.97	S.T.= 2.28		385,855.16
4	6	S 60°10'51.29" E	3.29	6	3,170,578.82
		CENTRO DE CURVA		5	3,170,590.83
		DELTA = 14°31'36.01"	L.C.= 3.30		385,863.42
		RADIO = 13.00	S.T.= 1.66		385,868.41
6	7	S 04°15'34.52" E	19.34	7	3,170,559.54
7	8	N 81°18'34.48" W	12.92	8	3,170,561.49
8	1	N 08°41'25.52" E	21.11	1	3,170,582.36
SUPERFICIE = 215.31 m2					

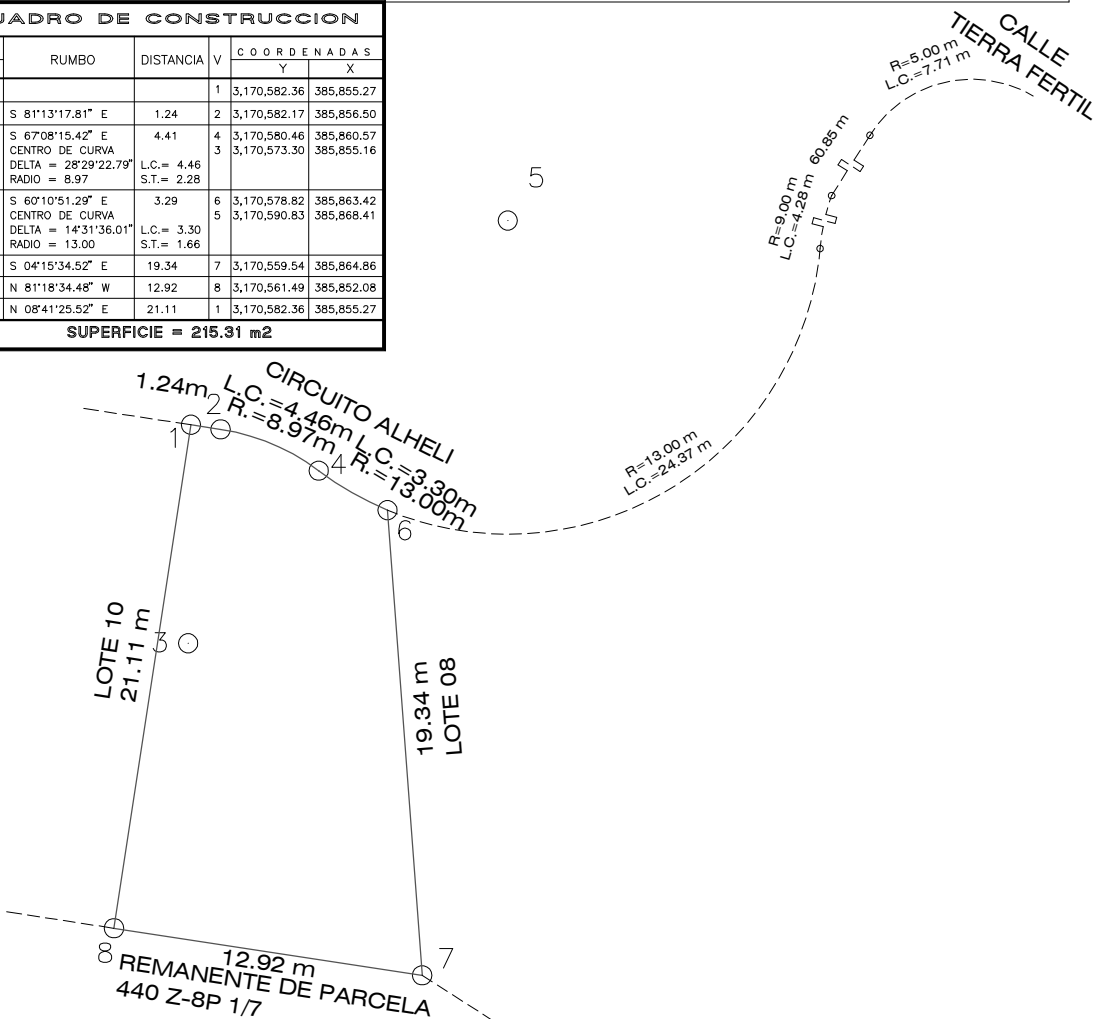

LOCALIZACIÓN

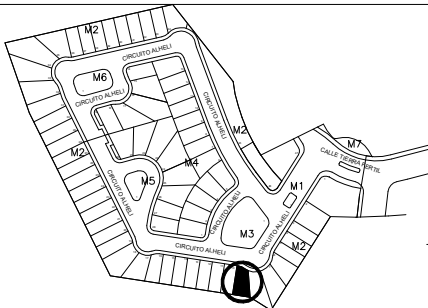

ING. JOSÉ LUIS RODRÍGUEZ HERNÁNDEZ
REG. P.C. No. 1899

CHIHUAHUA, CHIHUAHUA.
ENERO 2026